


67-73 QUEENS RD - EVERTON HILLS - DETAILED LANDSCAPE WORKS

DRAWING TITLE DRAWING NO.

Cover Sheet	D24066-CS-01
Detailed Landscape: Landscape Works Legend & Planting Schedule	D24066-LE-01
Detailed Landscape: General Notes & Specifications	D24066-LE-02
Detailed: Landscape Plan	D24066-LP-01
Detailed: Landscape Plan	D24066-LP-02
Detailed: Landscape Plan	D24066-LP-03
Detailed: Landscape Plan	D24066-LP-04
Landscape Details	D24066-DT-901
Landscape Details	D24066-DT-902

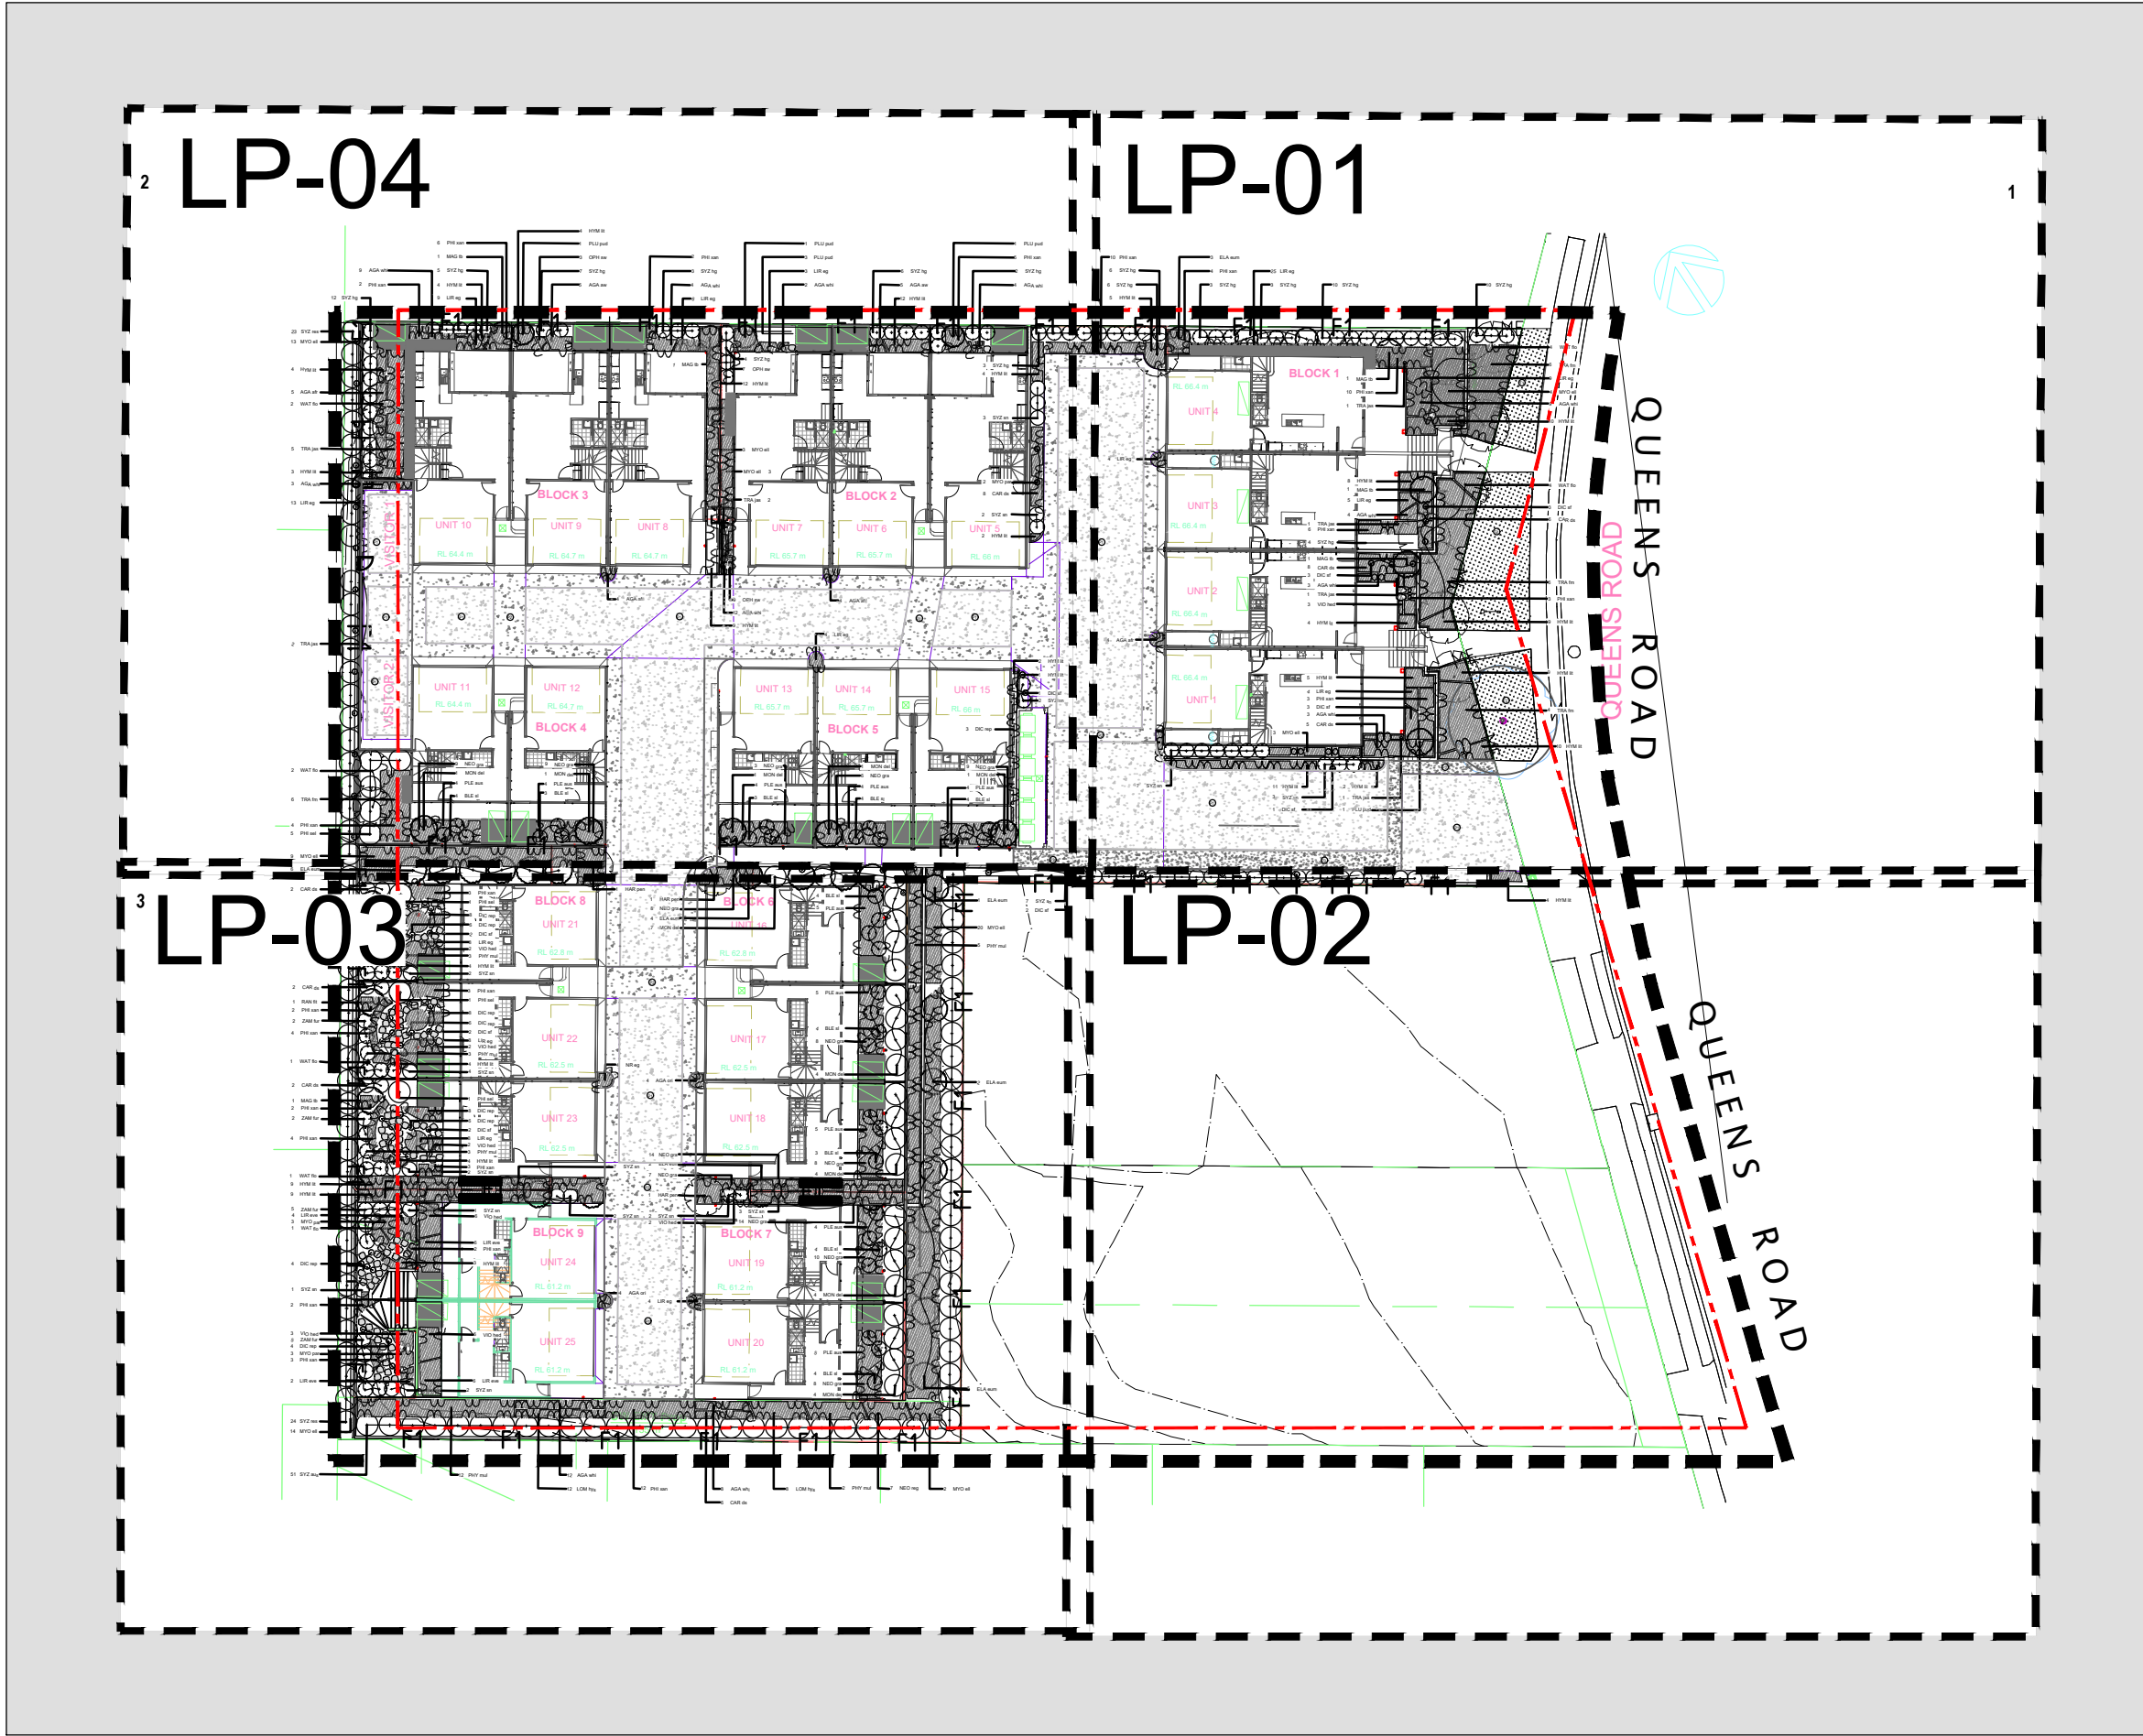

DRAWING OVERALL PLAN

SCALE 1:500 @A1
SCALE 1:1000 @A3

- EXTENT OF LANDSCAPE WORKS
- EXTENT OF LANDSCAPE WORKS

D23021-CS-001
ISSUE: A: FOR APPROVAL
DATE: XX DECEMBER, 2024

FOR: GROOVE PROPERTIES PTY LTD BY:

David Scassola AILA
REGISTERED LANDSCAPE ARCHITECT
Membership #: 001746
PH: 0407 589 785
EMAIL: david@thelandscapegroup.com.au
ABN: 83166834224

LANDSCAPE: GENERAL NOTES & SPECIFICATIONS

GENERAL NOTES:

1. ALL LANDSCAPE WORKS ARE TO BE UNDERTAKEN IN ACCORDANCE WITH M.B.R.C REQUIREMENTS.
2. SET OUT WORKS. ALL WORK TO BE SET OUT ON SITE FOR APPROVAL BY LANDSCAPE SUPERINTENDENT PRIOR TO CONSTRUCTION. NO WORK TO COMMENCE ON SITE WITHOUT PRIOR APPROVAL FROM LANDSCAPE SUPERINTENDENT. THE CONTRACTORS SCOPE OF WORKS ARE AS SHOWN WITHIN THE "EXTENT OF WORKS" DASHED LINE. REFER LANDSCAPE PLANS FOR FURTHER DETAIL. NO WORKS SHOULD BE UNDERTAKEN OUTSIDE THIS EXTENT OF WORKS LINE AT ANYTIME DURING THE PROJECT LIFE CYCLE.
3. ALL SERVICE LOCATIONS SHOWN ARE INDICATIVE ONLY. REFER TO ENGINEERS DRAWINGS FOR MORE DETAIL. CONFIRM SERVICE LOCATIONS ON SITE PRIOR TO ANY CONSTRUCTION. IT SHOULD BE NOTED THAT THESE LANDSCAPE DRAWINGS PRODUCED ARE TO BE READ IN CONJUNCTION WITH ALL DOCUMENTS FROM ALL OTHER CONSULTANTS INVOLVED.
4. THE LANDSCAPE CONTRACTOR SHALL CONFIRM THE LOCATION OF ALL UNDERGROUND SERVICES PRIOR TO COMMENCEMENT OF WORKS. THE CONTRACTOR IS ALSO RESPONSIBLE FOR VERIFYING EXISTING UNDERGROUND SERVICES PRIOR TO THE COMMENCEMENT OF WORKS. IF UNABLE TO CLEARLY ESTABLISH LOCATIONS OF UNDERGROUND SERVICES FOLLOW DIAL BEFORE YOU DIG PROCEDURES.
5. REFER CIVIL ENGINEERS DRAWINGS FOR LOCATIONS OF ALL DESIGNED CIVIL INFRASTRUCTURE. REFER TO CIVIL ENGINEERS DRAWINGS FOR FINISHED SURFACE LEVELS. THE CIVIL WORKS INFORMATION AS SHOWN / CONTAINED WITHIN THIS LANDSCAPE PACKAGE IS INDICATIVE ONLY AND SHOULD BE NOT USED FOR CONSTRUCTION PURPOSES.
6. REFER ELECTRICAL ENGINEERS DRAWINGS FOR LOCATIONS OF ALL DESIGNED ELECTRICAL INFRASTRUCTURE. REFER ELECTRICAL ENGINEERS DRAWINGS FOR LOCATIONS OF GENERAL ELECTRICAL RETICULATION, NBN INFRASTRUCTURE, PIT, PIPE LAYOUTS & LOCATIONS OF POWER POLES. THE ELECTRICAL WORKS INFORMATION AS SHOWN / CONTAINED WITHIN THIS LANDSCAPE PACKAGE IS INDICATIVE ONLY AND SHOULD BE NOT USED FOR CONSTRUCTION PURPOSES.
7. FINAL PLANTING LOCATIONS AND NUMBERS SUBJECT TO FINAL SERVICE LOCATIONS. REFER TO PLANTING PLAN FOR PLANTING DETAILS.
8. GRASS AND WEED GROWTH SHALL BE ERADICATED PRIOR TO COMMENCEMENT.
9. NOTES ON FIRE ANTS: TO PREVENT THE SPREAD OF FIRE ANTS, THE QUEENSLAND GOVERNMENT HAS IMPLEMENTED MOVEMENT CONTROLS IN AREAS OF QUEENSLAND (BIOSECURITY ZONES) WHERE THIS PEST SPECIES HAS BEEN DETECTED. THESE CONTROLS APPLY TO INDIVIDUALS AND COMMERCIAL OPERATORS, AND RESTRICT THE MOVEMENT OF MATERIALS THAT COULD CARRY FIRE ANTS WHICH INCLUDE SOIL, TURF, POTTED PLANTS, MULCH, BALED HAY OR STRAW, ANIMAL MANURES, MINING OR QUARRY PRODUCTS. BREACHES OF THESE CONTROLS CAN POTENTIALLY IMPACT THE COMMUNITY, ECONOMY AND THE ENVIRONMENT. PENALTIES FOR NON-COMPLIANCE WITH MOVEMENT CONTROLS WITHIN FIRE ANT BIOSECURITY ZONES APPLY UNDER THE BIOSECURITY ACT 2014. IF YOU ARE UNSURE OF YOUR OBLIGATIONS CONTACT THE RELEVANT QUEENSLAND STATE GOVERNMENT DEPARTMENT (BIOSECURITY QUEENSLAND, DEPARTMENT OF AGRICULTURE AND FISHERIES)
10. NOTES ON FIRE ANTS: AS OF 1 JULY 2016, THE MOVEMENT AND STORAGE OF MULCH, TURF OR POTTED PLANTS (FIRE ANT CARRIERS) WITHIN THE THREE FIRE ANT BIOSECURITY ZONES MUST COMPLY WITH MOVEMENT AND STORAGE CONTROL REQUIREMENTS AND RESTRICTIONS AS DETERMINED BY THE BIOSECURITY ACT 2014 AND THE BIOSECURITY REGULATION 2016.

NOTES STRUCTURAL ITEMS:

11. THE LANDSCAPE CONTRACTOR SHALL BE RESPONSIBLE FOR THE SUPPLY OF ENGINEERING DRAWINGS FOR ANY STRUCTURAL ITEMS AS REQUIRED. ALL STRUCTURAL ELEMENTS REQUIRING ENGINEERING CERTIFICATION/INSPECTION TO BE ARRANGED AND CARRIED OUT AT LANDSCAPE CONTRACTOR'S EXPENSE. COPIES OF STRUCTURAL CERTIFICATIONS ARE TO BE PROVIDED TO THE LANDSCAPE SUPERINTENDENT.

NOTES ON FENCING:

12. (F1): FENCE TYPE 1. 1800MM HIGH CHAINWIRE FENCE (INCLUDE VEHICLE GATES). FINISH: VINYL COATED. COLOUR: BLACK. REFER LANDSCAPE DRAWINGS FOR LOCATIONS. FENCING BY OTHERS REFER ARCHITECTURE DOCUMENTATION.

NOTES ON LOCKING RAIL:

13. (LR): LOCK RAIL. LOCK-RAIL TO OPEN SPACE. TO BE INSTALLED BY THE LANDSCAPE CONTRACTOR. LOCK-RAIL TO BE INSTALLED AS PER L.C.C'S SPECIFICATIONS AND STANDARD DRAWINGS. LOCK-RAIL TO BE INSTALLED AS PER LOCATION ON LANDSCAPE DRAWING AND/OR AS REQUIRED FOR SAFE VEHICLE ACCESS. LOCK-RAIL TO BE A HOT DIPPED GALVANISED FINISH. REFER LANDSCAPE DRAWINGS FOR LOCATIONS & LANDSCAPE DETAIL FOR FURTHER INFORMATION.

NOTES ON BOLLARDS:

14. (B1): HARDWOOD BOLLARDS. TO BE INSTALLED BY THE LANDSCAPE CONTRACTOR. HARDWOOD TIMBER BOLLARDS TO BE INSTALLED AS PER L.C.C'S SPECIFICATIONS AND STANDARD DRAWINGS. HARDWOOD TIMBER BOLLARDS TO BE INSTALLED AS PER LOCATIONS ON LANDSCAPE DRAWINGS. REFER LANDSCAPE DRAWINGS FOR LOCATIONS & LANDSCAPE DETAIL FOR FURTHER INFORMATION.
15. FINISH TO HARDWOOD BOLLARDS: CN OIL. APPLY MINIMUM 2 COATS. ALLOWING 24 HOURS BETWEEN DRYING.

NOTES ON CONCRETE PAVEMENTS:

16. ALL PAVEMENTS INCLUDING ROAD & FOOTPATHS ARE BY CIVIL. NOTE: ALL PAVEMENTS ARE NOT APART OF LANDSCAPE WORKS. REFER CIVIL ENGINEERS DWG'S & SPECIFICATIONS FOR FURTHER INFORMATION.

NOTES ON EDGING:

17. (CE): CONCRETE EDGING. (CONCRETE EDGING TO LOCATION OF TURF & GARDEN INTERFACES). 150MM (DEEP) X 200MM (WIDE) CONCRETE EDGING WITH 50MM DEPTH COMPACTED CRUSHER DUST. TO BE INSTALLED AS SHOWN ON LANDSCAPE PLANS. CONCRETE EDGE COLOUR: CHARCOAL. TO BE INSTALLED AS PER M.R.C'S SPECIFICATIONS AND STANDARD DRAWING. REFER LANDSCAPE DRAWINGS FOR LOCATIONS & LANDSCAPE DETAILS FOR FURTHER INFORMATION. REFER DRAWING: STANDARD TYPICAL CONCRETE GARDEN EDGING. DRG NO: A4-00420. REV.C. DATE: 31.03.14.

NOTES ON IRRIGATION:

18. DESIGN AND CONSTRUCT IN COLLABORATION WITH IRRIGATION SPECIALIST AND BUILDER. PROVIDE FULLY AUTOMATIC IRRIGATION SYSTEM WITH SPRAY HEADS TO PROVIDE FULL COVERAGE TO GARDEN AND TURF AREAS. 1X IRRIGATION CONTROL STATION REQUIRED. NOTE: BACKFLOW PREVENTION DEVICE REQUIRED.

NOTES ON SURFACE DRAINAGE:

19. WHEN SETTING OUT LINES AND LEVELS OF GARDENS AND TURFED AREAS, ENSURE THE ACCURATE FORMATION OF GRADES AND CROSS FALLS LEADING TO SURFACE CATCH DRAINS AND FIELD INLETS; SO ENABLING THE AREAS TO DRY QUICKLY AND SURPLUS WATER TO REACH THE DRAINAGE SYSTEM IN SUCH A WAY THAT POTENTIAL EROSION CHANNELS AND/OR WET SPOTS ARE AVOIDED.

NOTES ON ROOT BARRIER:

20. ROOT BARRIER TO BE INSTALLED TO ENVIRONMENTAL COVENANT AND BIO-BASIN INTERFACE, AS SHOWN ON LANDSCAPE PLANS. MINIMUM 900MM DEEP ROOT BARRIER TO BE TRENCHED AND SECURED IN PLACE WITH 20 DIA DRAINAGE GRAVEL.

NOTES ON TOPSOIL:

21. IMPORTED TOPSOIL TO ALL LOCATIONS OF TURF. TO BE LAID ON 100MM DEPTH IMPORTED TOPSOIL. IMPORTED TOPSOIL TO COMPLY WITH AS4419 - 2003.
22. INSTALL ALL IMPORTED TOPSOIL TO A DEPTH OF 300MM AS DETAILED. TO ALL GARDEN BEDS. IMPORTED TOPSOIL TO COMPLY WITH AS4419 - 2003
23. SITE SOIL PRIOR TO USE NEEDS TO BE TESTED AND COMPLY WITH AS4419 - 2003 AND NUTRIENT LEVELS AS PER AS3743 - 2003.

NOTES ON MULCH:

24. MULCH UNDER ALL INDIVIDUAL STREET TREES IN TURF. 100MM LAYER OF MULCH UNDER ALL TREES. TO CONSIST OF 25MM HOOP PINE MULCH.
25. MULCH TO ALL GARDEN BEDS. 100MM LAYER TO ALL PLANTING BEDS. TO CONSIST OF 25MM HOOP PINE MULCH.
26. ENSURE MULCH IS PULLED AWAY FROM THE BASE / STEM OF ALL TREES TO PREVENT COLLAR ROT.

NOTES ON PLANTING AND PLANT SCHEDULE:

27. THE PLANT SCHEDULE IS PROVIDED FOR INFORMATION PURPOSES ONLY. THE CONTRACTOR SHALL REVIEW PLANT SCHEDULE TO ENSURE THE DRAWINGS AND SCHEDULE CONCUR. WHERE DISCREPANCIES EXIST, NUMBERS INDICATED ON DRAWINGS SHALL TAKE PRECEDENCE.
28. ALL STREET TREES ARE TO BE NAT-SPEC COMPLIANT AND CERTIFICATES TO BE SUPPLIED BY ARBORIST/NURSERY PRIOR TO INSTALLATION ON SITE. THE LANDSCAPE SUPERINTENDENT RESERVES THE RIGHT TO DEFECT ANY PLANT STOCK THAT IS NOT DEEMED TO MEET REQUIREMENTS, TO BE REPLACED AT CONTRACTOR'S COST.
29. SINGULAR STREET TREES ARE TO BE INSTALLED WITH 100MM MULCH CONSISTING OF, IMPORTED DOUBLE TUB GROUND MULCH. WITH A SPADE EDGE TO TURF AND MULCH INTERFACES. ALL INTERNAL STREET TREES TO BE INSTALLED AS PER LOCATIONS SHOWN ON LANDSCAPE PLANS FOR STAGE 2.
30. CONTAINER AND HEIGHT SIZES SHOWN ARE MINIMUM ACCEPTABLE SIZES.
31. SPECIES AND SIZES SUBSTITUTIONS MAY BE ACCEPTED, TO BE CONFIRMED WITH LANDSCAPE SUPERINTENDENT IN WRITING PRIOR TO ORDERING / INSTALLATION.
32. GRASS SPECIES ARE TO BE PLANTED WITH CROWN OF PLANT CLEAR OF MULCH.
33. REFER ABOVE AND BELOW TO LANDSCAPE SPECIFICATIONS FOR ALL SOIL AND MULCH REQUIREMENTS.

34. PLANTING AREAS SHALL CONSIST OF:

- 150MM MINIMUM CULTIVATED SUB-GRADE.
- PRIOR TO CULTIVATING SUB-GRADE APPLY GYPSUM AS PER MANUFACTURE'S RECOMMENDATIONS. FOLLOWING THE APPLICATION OF GYPSUM, SPREAD BLOOD AND BONE OR SIMILAR TO MANUFACTURES RECOMMENDATIONS PRIOR TO SPREADING TOPSOIL.
- TOP SOIL AS SPECIFIED ABOVE.
- MULCH AS SPECIFIED ABOVE.
- SUBSOIL DRAINAGE AS REQUIRED FOR STORM-WATER. IF SUBSOIL DRAINAGE IS REQUIRED. SUBSOIL DRAINS TO BE 100 DIA FLEXIBLE AGG, DRAIN WRAPPED IN GEO-TEXTLE SOCK.

NOTES ON PLANT MATERIAL QUALITY AND SPECIFICATION OF NURSERY STOCK:

42. ALL PLANTS SHALL BE TRUE TO SCHEDULED NOMENCLATURE, WELL FORMED, HARDENED OFF AND DISEASE FREE NURSERY STOCK. THEY SHALL BE CONTAINER GROWN IN POTTING SOIL WITH ROOT SYSTEM FIRMLY ESTABLISHED BUT WITH NO LARGE ROOTS GROWING OUT OF THE CONTAINER. NO PLANT SHALL BE POT BOUND.
43. EXCAVATE OR FILL AREAS AS NECESSARY ALLOWING FOR DEPTHS OF MODIFIED SITE SOIL AND MULCH. REMOVE AND DESTROY ANY GRASS OR WEED GROWTH PRESENT. IF NOXIOUS WEEDS ARE FOUND, SUCH AS NUT GRASS, IN THE AREA TO BE CULTIVATED AND PREPARED, INFORM THE SUPERINTENDENT BEFORE PROCEEDING.
44. DECOMPACT EXISTING GROUND TO A MINIMUM OF 100MM. IN AREAS OF CUT OR WHERE COMPACTION OF THE SUB-GRADE HAS OCCURRED DEEP RIP SUB-GRADE TO MINIMUM DEPTH OF 100MM.
45. CARRY OUT ANY SUB-SURFACE DRAINAGE WORKS AS REQUIRED.
46. SPREAD SOIL AS SPECIFIED TO DEPTHS AS SHOWN IN DETAILS ENSURING MINIMUM THICKNESS SHOWN ON DRAWINGS AFTER SETTLEMENT.
47. AS THE GROUND IS WORKED, ALL GARDEN AREAS ARE TO BE RAISED OR CROWNED IN THE CENTER TO ASSIST IN SOIL DRAINAGE UNLESS IN A DESIGNATED OVERLAND FLOW PATH.
48. FINISHED LEVEL OF SOIL AT PATHS TO ALLOW FOR SETTLEMENT AND FOR THE PLACEMENT OF MULCH OR TURF AS SPECIFIED.

STREET TREE:

49. STREET TREE CLEARANCE DISTANCES:

(a) 4 METRES FROM ELECTRICITY OR TELECOMMUNICATION POLES OR PILLARS;

(b) 7.5 METRES FROM STREETLIGHTS TO ENSURE EFFECTIVE STREET LIGHTING;

(c) 4 METRE RADIUS FROM HIGH VOLTAGE TRANSMISSION LINES;

(d) 3 METRES FROM A FIRE HYDRANT;

(e) 1 METRE FROM STORMWATER DRAINAGE PIT OR GULLY DRAIN;

(f) 3 METRES FROM A DRIVEWAY;

(g) 10 METRES FROM THE FACE OF THE KERB OF THE ADJOINING STREET AT AN INTERSECTION; AND

(h) 6 METRES FROM THE DEPARTURE SIDE OF BUS STOPS AND PEDESTRIAN CROSSINGS.
50. ALL STREET TREES ARE TO HAVE A MINIMUM CLEAR TRUNK HEIGHT OF 1500mm AT MATURITY UNLESS OTHERWISE APPROVED BY COUNCIL.
51. ALL STREET TREES BETWEEN KERB AND FOOTPATH IS TO BE A MINIMUM OFFSET OF 750mm.
52. ALL STREET TREES TO INCLUDE TREE EDGING INSTALLED AT 1200mm X 1200mm AROUND MULCHED BED.

NOTES ON TURFING AND TURF SUPPLY:

53. OBTAIN TURF FROM A SPECIALIST GROWER OF CULTIVATED TURF.
54. (T1): TURF TYPE 1. TO ALL ROAD VERGES AND INTERNAL AREAS, REFER PLANS FOR MINIMAL EXTENT. 'A GRADE' WINTERGREEN: NATURAL TURF.
55. (MGT): MAKE GOOD TURF. TO ALL DISTURBED AREAS, REFER PLANS FOR MINIMAL EXTENT. 'A GRADE' WINTERGREEN: NATURAL TURF.
56. TURF TO BE FREE FROM NUT-GRASS OR OTHER NOXIOUS WEEDS OR ANY OTHER MATERIAL DELETERIOUS TO PLANT GROWTH. ENSURE TURF IS WEED FREE AT THE END OF THE MAINTENANCE PERIOD.
57. DELIVER THE TURF WITHIN 24 HOURS OF CUTTING, AND LAY IT WITHIN 36 HOURS OF CUTTING. PREVENT IT FROM DRYING OUT BETWEEN CUTTING AND LAYING.
58. TURF TO BE LAID ON IMPORTED TOPSOIL INSTALLED BY LANDSCAPE CONTRACTOR TO 100MM DEPTH.
59. LIGHTLY ROLL AFTER LAYING TURF. TOP-DRESS AS NECESSARY TO REMOVE UNDULATIONS AND THE LIKE. ALL TURF AREAS TO HAVE A MINIMUM 1:50 CROSS-FALL TO ENSURE ALL TURF IS WELL DRAINED. WATER IMMEDIATELY AFTER INSTALLATION, UNTIL THE TOPSOIL IS MOISTENED TO ITS FULL DEPTH.
60. BEFORE TURFING, APPLY FERTILISER OF 14:15:10 N.P.K. OR APPROVED SIMILAR COMPOSITION AT THE RATE OF 100G PER M2 AND RAKE INTO THE PREPARED SOIL.

INTERNAL LANDSCAPE WORKS MAINTENANCE:

61. LANDSCAPE ESTABLISHMENT: WILL OCCUR OVER PERIOD OF 12 WEEKS AND SHALL APPLY FOR ALL LANDSCAPE WORKS. THE 12 WEEK ESTABLISHMENT PERIOD SHALL INCLUDE WEEDING, WATERING, PRUNING AND RE-MULCHING. PLANTS NOT SHOWING SIGNS OF ACTIVE GROWTH AT THE END OF THE ESTABLISHMENT PERIOD SHALL BE REPLACED BY THE CONTRACTOR.

STREETSCAPE WORKS MAINTENANCE:

62. STREETSCAPE WORKS: LANDSCAPE ESTABLISHMENT MAINTENANCE. AN ESTABLISHMENT PERIOD OF (12) WEEKS, (3) MONTHS FROM SATISFACTORY PRACTICAL COMPLETION INSPECTION SHALL APPLY FOR ALL LANDSCAPE WORKS. THE 12 WEEK ESTABLISHMENT PERIOD SHALL INCLUDE MOWING, WEEDING, WATERING, PRUNING AND RE-MULCHING. PLANTS NOT SHOWING SIGNS OF ACTIVE GROWTH AT THE END OF THE ESTABLISHMENT PERIOD SHALL BE REPLACED BY THE CONTRACTOR.
63. STREETSCAPE WORKS: LANDSCAPE MAINTENANCE. AN ON MAINTENANCE PERIOD OF (52) WEEKS, (12) MONTHS SHALL COMMENCE FROM COUNCIL ON MAINTENANCE ACCEPTANCE. THIS WILL OCCUR OVER A PERIOD OF (12) MONTHS AND SHALL APPLY FOR ALL LANDSCAPE WORKS. THIS WILL BE AN ONGOING PERIOD OF WORKS INCLUDING BUT NOT LIMITED TO MOWING, WEEDING, WATERING, PRUNING AND RE-MULCHING. PLANTS NOT SHOWING SIGNS OF ACTIVE GROWTH AT THE END OF THE 38TH WEEK WITHIN THE MAINTENANCE PERIOD SHALL BE REPLACED BY THE CONTRACTOR

67-73 QUEENS RD
EVERTON HILLS

For

GROOVE PROPERTIES
PTY LTD

IMPORTANT NOTES:
This plan was prepared for GROOVE PROPERTIES PTY LTD and should not be used for any other purpose.

The dimensions, areas and total number of lots shown hereon are subject to final field survey and also to the requirements of Council and any other authority which may have requirements under any relevant legislation.

The Contours, boundaries, creek line, flood lines, building locations have all been scaled and should not have any reliance based on them as they are only intended as a general guide. The configuration of allotments shown on this plan is subject to Local Authority (and relevant State Government Authority) approvals, detailed design, final survey, and registration of survey plans.

Any comments contained on this plan should be confirmed by the relevant authorities. In particular, no relevance should be placed on the information on this plan for any financial dealings involving the land.

(C) COPYRIGHT THE LANDSCAPE GROUP: 2024

THESE DESIGNS AND DRAWINGS ARE COPYRIGHT AND ARE NOT TO BE USED OR REPRODUCED WITHOUT THE WRITTEN PERMISSION OF THE LANDSCAPE GROUP

REFER TO ARCHITECTURAL & ENGINEERING DRAWINGS FOR LOCATIONS OF SERVICES

A	Design Issue	XX.12.2024	DS
No	Revisions	Date	Chkd

Locality: EVERTON HILLS
Local Authority: M.B.R.C
Scale:

Drawn: KD
Checked: DS
Plot Date: XX DEC, 2024
Computer File Ref: D23021-LP-A.dwg

DETAILED LANDSCAPE
WORKS

LEGEND
&
PLANTING PALETTE

The

LANDSCAPE

GROUP

David Scassola AILA
REGISTERED LANDSCAPE ARCHITECT
Membership #: 001846
PH: 0407 589 785
EMAIL: david@thelandscapegroup.com.au
ABN: 83166834224

Drawing No

D24066-LE-001

Issue

A

LANDSCAPE WORKS: LEGEND

EXTENT OF WORKS:
REFER TO PLANS FOR LOCATIONS.

PROPERTY BOUNDARY -
REFER TO PLANS FOR LOCATIONS.

LANDSCAPE TREES:
REFER TO PLANTING LISTS & PLANS FOR LOCATIONS.

LANDSCAPE TREES:
REFER TO PLANTING LISTS & PLANS FOR LOCATIONS.

GROUND COVER PLANTS:
REFER TO PLANTING LISTS & PLANS FOR LOCATIONS.

TRELLIS: STAINLESS STEEL WIRE -
REFER PLANS FOR LOCATION AND DETAILS.

BABYLON STONE PAVERS
SUPPLIER: CENTENARY LANDSCAPING SUPPLIES

(ME) METAL EDGE: GALVANISED STEEL -
FINISH: GALVANISED STEEL EDGE, POWDER COATED BLACK. PRODUCT: FORMBOSS 75MM
EDGING - OR APPROVED EQUIVALENT. REFER PLANS FOR LOCATIONS

(T1) TURF TYPE 1: 'A GRADE' WINTERGREEN (NATURAL TURF) -
REFER PLANS FOR LOCATIONS
NATURAL TURF: CENTENARY LANDSCAPES.

(F1): FENCE TYPE 1. 1800MM HIGH. DOUBLE LAP JOINTED & CAPPED TIMBER FENCE - BY OTHERS
REFER PLANS FOR LOCATIONS

(F2): FENCE TYPE 2. 1800MM HIGH. DOUBLE LAP JOINTED & CAPPED TIMBER ACOUSTIC FENCE - BY OTHERS
REFER PLANS FOR LOCATIONS

GATE: TYPE VARIES -
REFER PLANS FOR LOCATIONS AND ADJOINING FENCE TYPES.

CLOTHESLINE: FIXED TO FENCE -
AUSTRAL 3.3M. WOODLAND GREY. SLENDERLINE 20 FOLD DOWN SINGLE CLOTHESLINE. BUNNINGS WAREHOUSE
REFER PLANS FOR LOCATIONS

LANDSCAPE WORKS: MATERIAL SCHEDULE

67-73 QUEENS RD, EVERTON HILLS. Materials & Finishes Schedule Note: <i>*Material substitutions will not be accepted unless prior authorisation has been arranged & discussed with the Landscape Architect.</i> <i>* Material & Finishes as shown below may not be changed unless prior authorisation has been arranged & discussed with the Landscape Architect.</i> <i>*All landscape works to be installed, as per detailed landscape drawing.</i>			
Item	Description	Finish & Colour	Manufacturer & Supplier
Surface Finishes			
(G1) Gravel Type 1	General: - Caramel Swirl 10mm - 50mm depth - Geotextile underlay	N/A	Nuway Landscape Supplies (07) 3390 2477
(P1) Paver Type 1	General: -In Situ concrete steppers Material: - Tiles as per pool surrounds	Finish: Refer to Architects drawings	Refer to Architects drawings
Furniture Items			
Access Ladder	General: - Steel Access Ladder, 900mm long, permanently fixed to the fence/wall Material: - Galvanised Steel Rigid	Finish: Galvanised Steel	Contractors Choice
Fencing			

LANDSCAPE WORKS: PLANTING SCHEDULE

D24066 - QUEENS RD EVERTON HILLS PLANTING LIST NOTE: *Plant substitutions will not be accepted, unless prior authorisation has been arranged & disscussed with Landscape Architect. * Plant sizes as shown may not be changed,unless prior authorisation has been arranged & disscussed with Landscape Architect. *All landscape planting works to be installed, as per detailed landscape drawing. Any planting changes, in numbers, sizes & substitutions will not be accepted unless prior authorisation has been arranged & disscussed with Landscape Architect.				
TREES				
KEY	SCIENTIFIC NAME	COMMON NAME	SIZE	NUMBERS
CUP ana	Cupaniopsis anacardioides	Tuckeroo	100L	
ELA eum	Elaeocarpus eumundi	Eumundi Quandong	100L	
FLI aus	Flindersia australis	Australian Teak	45L	
HAR pen	Harpullia pendula	Tulipwood	100L	
RAN fit	Randia fitzalanii	Native Gardenia	45L	
XAN chr	Xanthostemon chrysanthus	Golden Penda	45L	
MAG teb	Magnolia grandiflora 'teddy bear'	Magnolia teddy bear	45L	
WAT flo	Waterhousia Floribunda			
PLU pud	Plumeria Pudica			
			TOTAL	0
SHRUBS				
KEY	SCIENTIFIC NAME	COMMON NAME	SIZE	NUMBERS
ALP nut	Alpinia nutans	Dwarf Ginger	140mm	
CAR mac	Carissa macrocarpa 'Desert Star'	Natal Plum	140mm	
CYA coo	Cyathea cooperi	Australian Tree Fern	200mm	
DIO spi	Dioon spinulosum	Giant Dioon	400mm	
GRE fla	Grevillea Winter Flame	Spider Flower	140mm	
GRE won	Grevillea 'Winter Wonder'	Woolly Grevillea	140mm	
KAL ss	Kalanchoe 'Silver Spoons'	Silver Spoons	200mm	
MON del	Monstera deliciosa	Swiss Cheese Plant	300mm	
DOR exc	Doryanthes excelsa	Gymea Lilly	300mm	
SYZ res	Syzygium resilience	Lilly pilly	200mm	
PHI xan	Philodendron xanadu	Xanadu	140mm	
PIT mis	Pittosporum Miss Muffet	Dwarf Pittosporum	140mm	
PIT ivo	Pittosporum tenuifolium Ivory Pillar	Kohuhu	140mm	
PHI xan	Philodendron xanadu	Xanadu	140mm	
PHI sel	Philodendron selloum	Lace Tree Philodendron	300mm	
RHA cos	Rhaphiolepis 'Cosmic White'	Cosmic White Hawthorn	200mm	
RHA sno	Rhaphiolepis 'Snow Maiden'	Snow Maiden Hawthorn	200mm	
RHA exc	Rhapis excelsa	Lady palm	200mm	
VIB el	Viburnum 'Emerald Lustre'	Emerald Lustre	200mm	
WES zen	Westringia fruticosa Zena	Compact Coastal Rosemary	200mm	
ZAM fur	Zamia furfurea	Cardboard Palm	200mm	
			TOTAL	0
GROUNDCOVERS/CLIMBERS				
KEY	SCIENTIFIC NAME	COMMON NAME	SIZE	NUMBERS
AGA afr	Agapanthus africanus 'white'	African Lily	140mm	
BLE sl	Blechnum 'Silver Lady'	Silver Lady	140mm	
DIC rep	Dichondra repens	Kidney Weed	140mm	
DIC sil	Dicondra Argentea 'Silver Falls'	Kidney Weed	140mm	
FIC pum	Ficus pumila	Climbing Fig	140mm	
FIC gre	Ficus microcarpa Green Island	Green Island Fig	140mm	
LIR eve	Liriope muscari 'Evergreen Giant'	Liriope 'Evergreen Giant'	140mm	
LOM hys	Lomandra hystix	Mat rush	140mm	
LOM sha	Lomandra shara	Shara	140mm	
PLE aus	Plectranthus australis	Swedish Ivy	140mm	
MYO par	Myoporum parvifolium purpurea	Boobialla	140mm	
NEO gra	Neomarica gracilis	Walking Iris	140mm	
NEO reg	Neomarica caerulea Regina	Giants Apostles Iris	140mm	
PHL aur	Phlebodium aureum	Blue Star Fern	140mm	
PYR ven	Pyrostegia venusta	Orange Trumpet Vine	140mm	
SEN er	Senecio serpens	Blue Chalk Sticks	140mm	
VIO hed	Viola hederacea	Native Violet	140mm	
TRA tri	Trachelospermum 'Tricolour'	Variegated Star Jasmine	140mm	
			TOTAL	0

67-73 QUEENS RD
EVERTON HILLS

For

GROOVE PROPERTIES
PTY LTD

IMPORTANT NOTES:
This plan was prepared for GROOVE PROPERTIES PTY LTD and should not be used for any other purpose.

The dimensions, areas and total number of lots shown hereon are subject to final field survey and also to the requirements of Council and any other authority which may have requirements under any relevant legislation.

The Contours, boundaries, creek line, flood lines, building locations have all been scaled and should not have any reliance based on them as they are only intended as a general guide. The configuration of allotments shown on this plan is subject to Local Authority (and relevant State Government Authority) approvals, detailed design, final survey, and registration of survey plans.

Any comments contained on this plan should be confirmed by the relevant authorities.
In particular, no relevance should be placed on the information on this plan for any financial dealings involving the land.

(C) COPYRIGHT THE LANDSCAPE GROUP: 2024

THESE DESIGNS AND DRAWINGS ARE COPYRIGHT AND ARE NOT TO BE USED OR REPRODUCED WITHOUT THE WRITTEN PERMISSION OF THE LANDSCAPE GROUP

REFER TO ARCHITECTURAL & ENGINEERING DRAWINGS FOR LOCATIONS OF SERVICES

A	Design Issue	XX.12.2024	DS
No	Revisions	Date	Chkd

Locality: EVERTON HILLS
Local Authority: M.B.R.C
Scale:

Drawn: KD
Checked: DS
Plot Date: XX DEC, 2024
Computer File Ref: D23021-LP-A.dwg

DETAILED LANDSCAPE
WORKS

LEGEND
&
PLANTING PALETTE

The

LANDSCAPE

GROUP

David Scassola AILA
REGISTERED LANDSCAPE ARCHITECT
Membership #: 001846
PH: 0407 589 785
EMAIL: david@thelandscapegroup.com.au
ABN: 83166834224

Drawing No

D24066-LE-002

Issue

A

(C) COPYRIGHT THE LANDSCAPE GROUP: 2024

**REFER TO ARCHITECTURAL & ENGINEERING
DRAWINGS FOR LOCATIONS OF SERVICES**

[illegible]


A	Design Issue	XX.12.2024	DS
No	Revisions	Date	Chkd

Drawn: KD
Checked: DS
Plot Date: XX DEC, 2024
Computer File Ref: D23021-LP-A.dwg

LANDSCAPE PLAN
SHEET 01 OF 02



Drawing No	Issue
D24066-LP-01	A

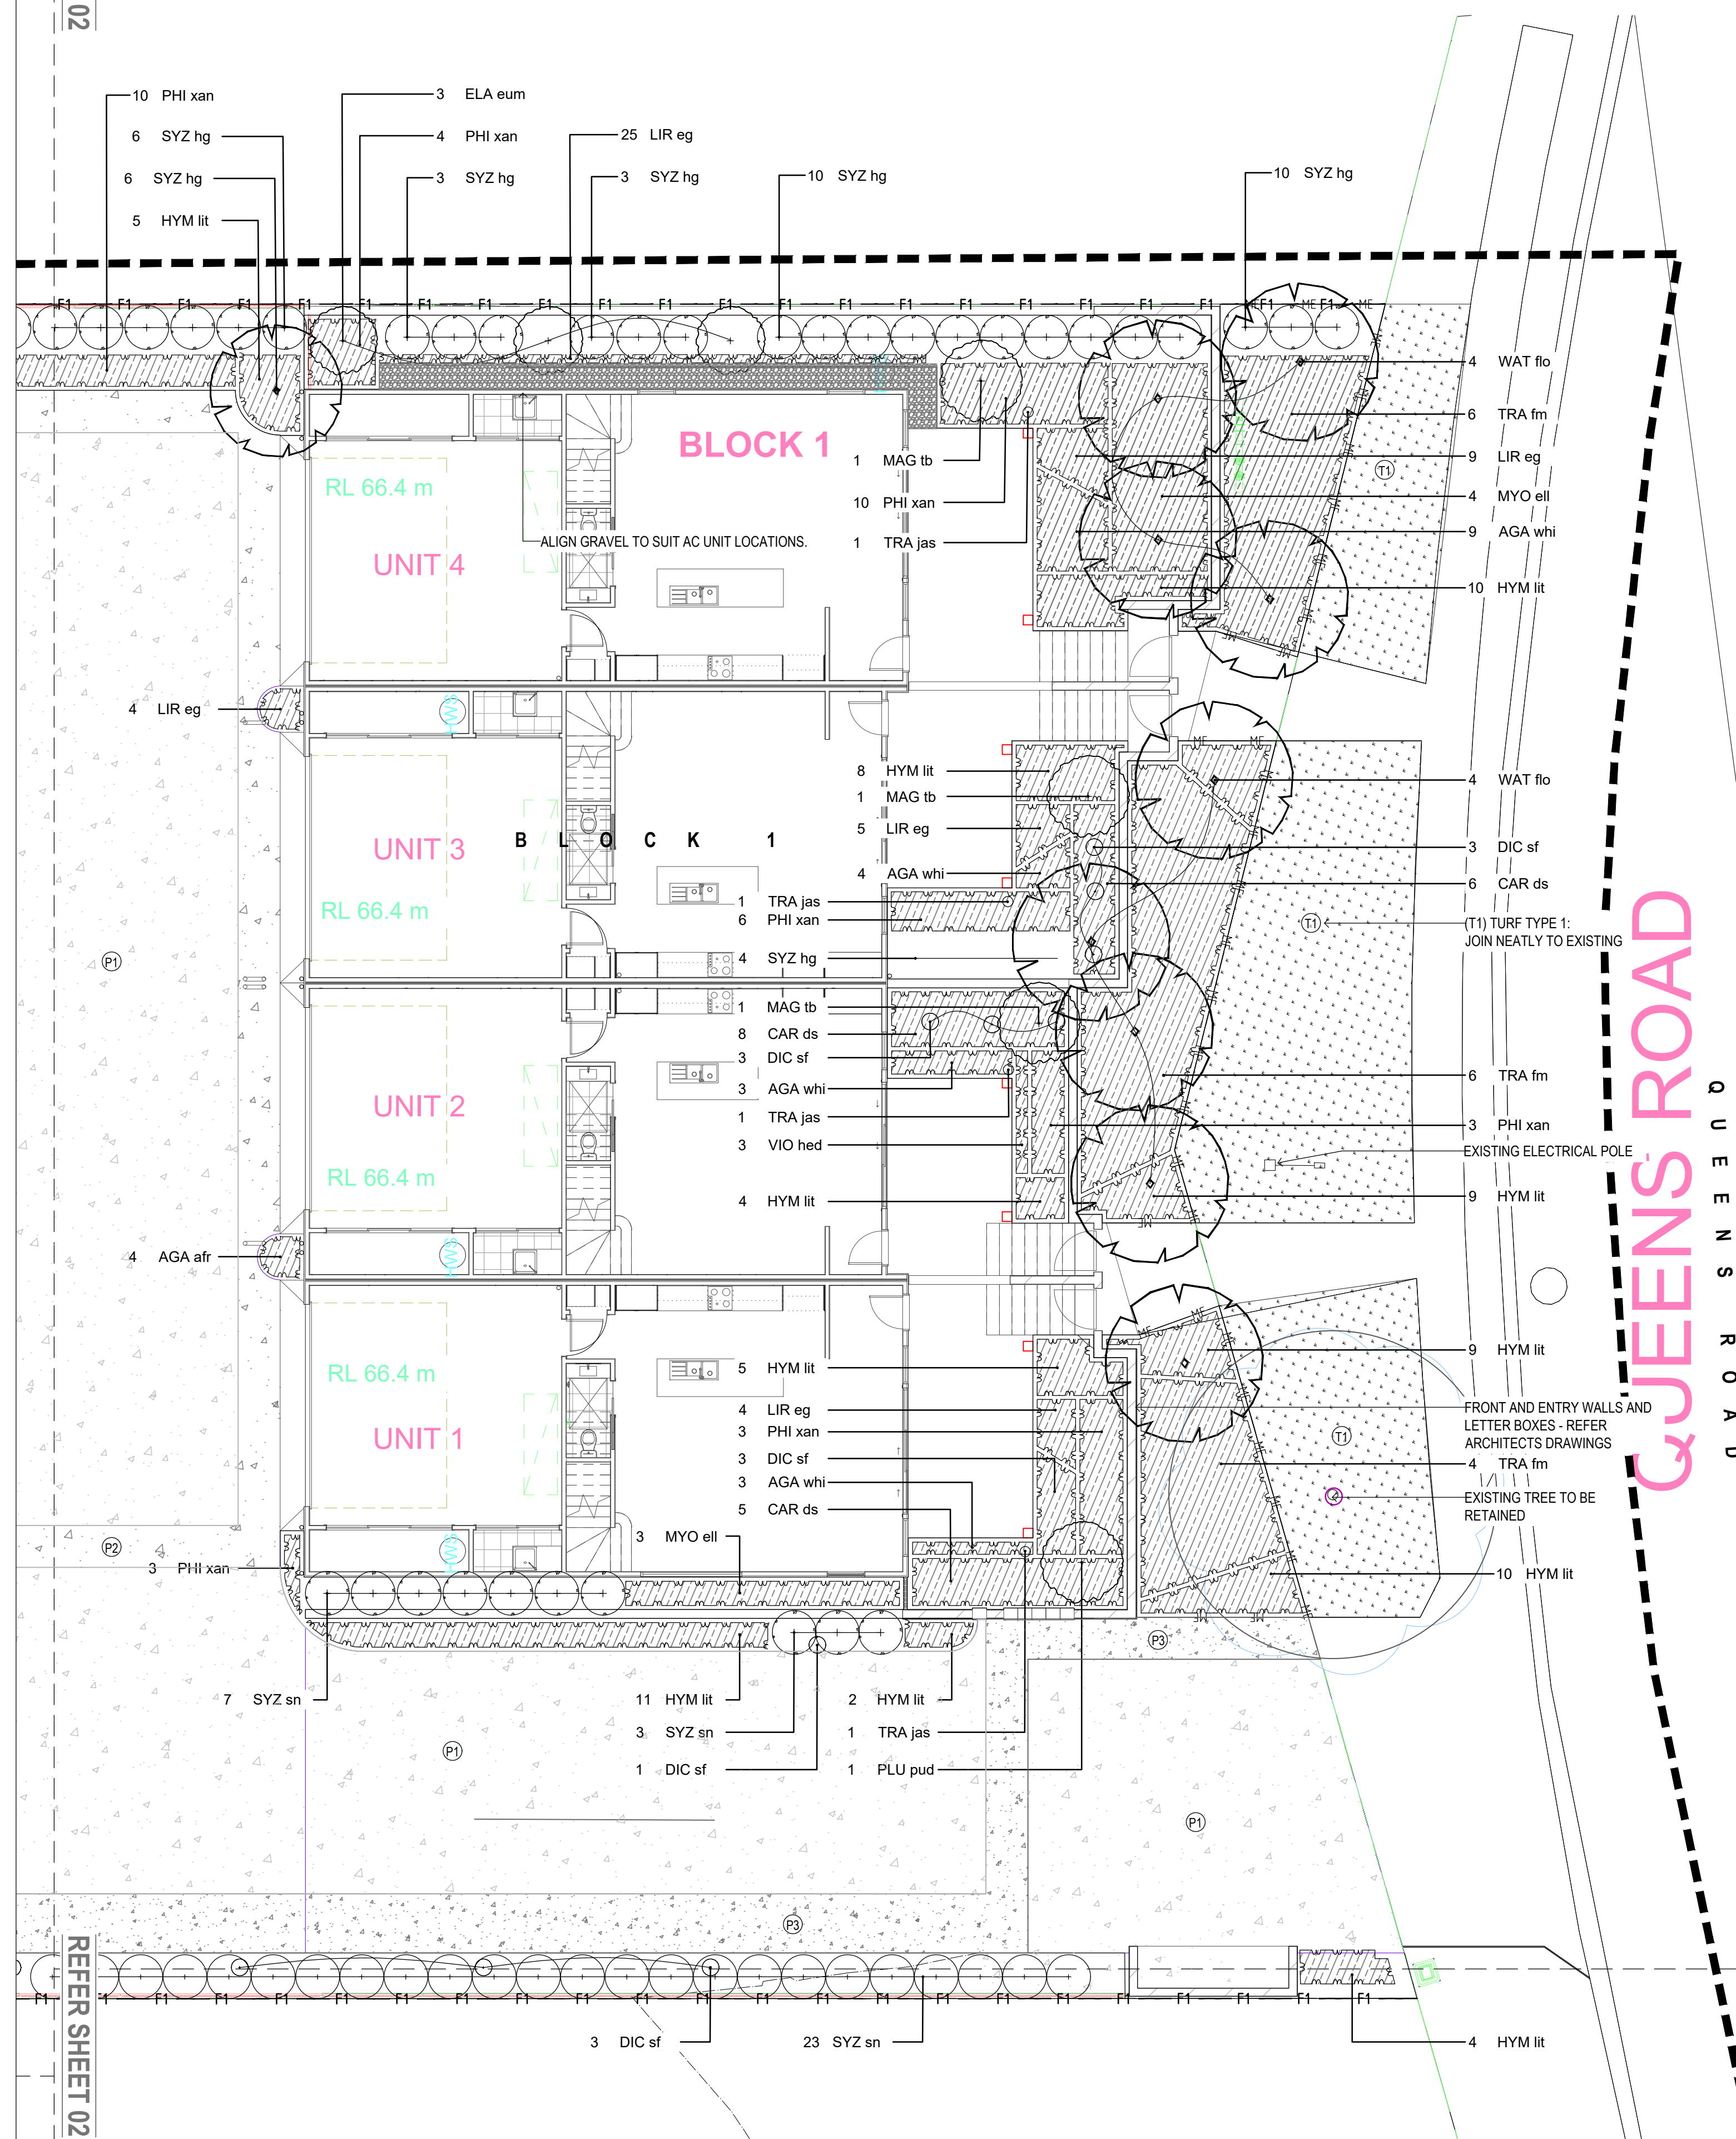



Drawing No	Issue
D24066-LP-02	A

9

For

IMPORTANT NOTES:
This plan was prepared for GROOVE PROPERTIES PTY LTD
and should not be used for any other purpose.

The dimensions, areas and total number of lots shown hereon are subject to final field survey and also to the requirements of Council and any other authority which may have requirements under any relevant legislation.

The Contours, boundaries, creek line, flood lines, building locations have all been scaled and should not have any reliance based on them as they are only intended as a general guide. The configuration of allotments shown on this plan is subject to Local Authority (and relevant State Government Authority) approvals, detailed design, final survey, and registration of survey plans.

Any comments contained on this plan should be confirmed by the relevant authorities.
In particular, no relevance should be placed on the information on this plan for any financial dealings involving the land.

(C) COPYRIGHT THE LANDSCAPE GROUP: 2024

**THESE DESIGNS AND DRAWINGS ARE COPYRIGHT
AND ARE NOT TO BE USED OR REPRODUCED
WITHOUT THE WRITTEN PERMISSION OF THE
LANDSCAPE GROUP**

**REFER TO ARCHITECTURAL & ENGINEERING
DRAWINGS FOR LOCATIONS OF SERVICES**

[illegible]

A	Design Issue	XX.12.2024	DS
No	Revisions	Date	Chkd

Locality: EVERTON HILLS
Local Authority: M.B.R.C
Scale: 1:100 @ A1
1:200 @ A3

Drawn: KD
Checked: DS
Plot Date: XX DEC, 2024
Computer File Ref: D23021-LP-A.dwg

DETAILED LANDSCAPE WORKS

**LANDSCAPE PLAN
SHEET 01 OF 02**




David Scassola AILA
REGISTERED LANDSCAPE ARCHITECT
Membership #: 001846
PH: 0407 589 785
EMAIL: david@thelandscapegroup.com.au
ABN: 83166834224

Drawing No
D24066-LP-03

Issue

A

REFER SHEET 02

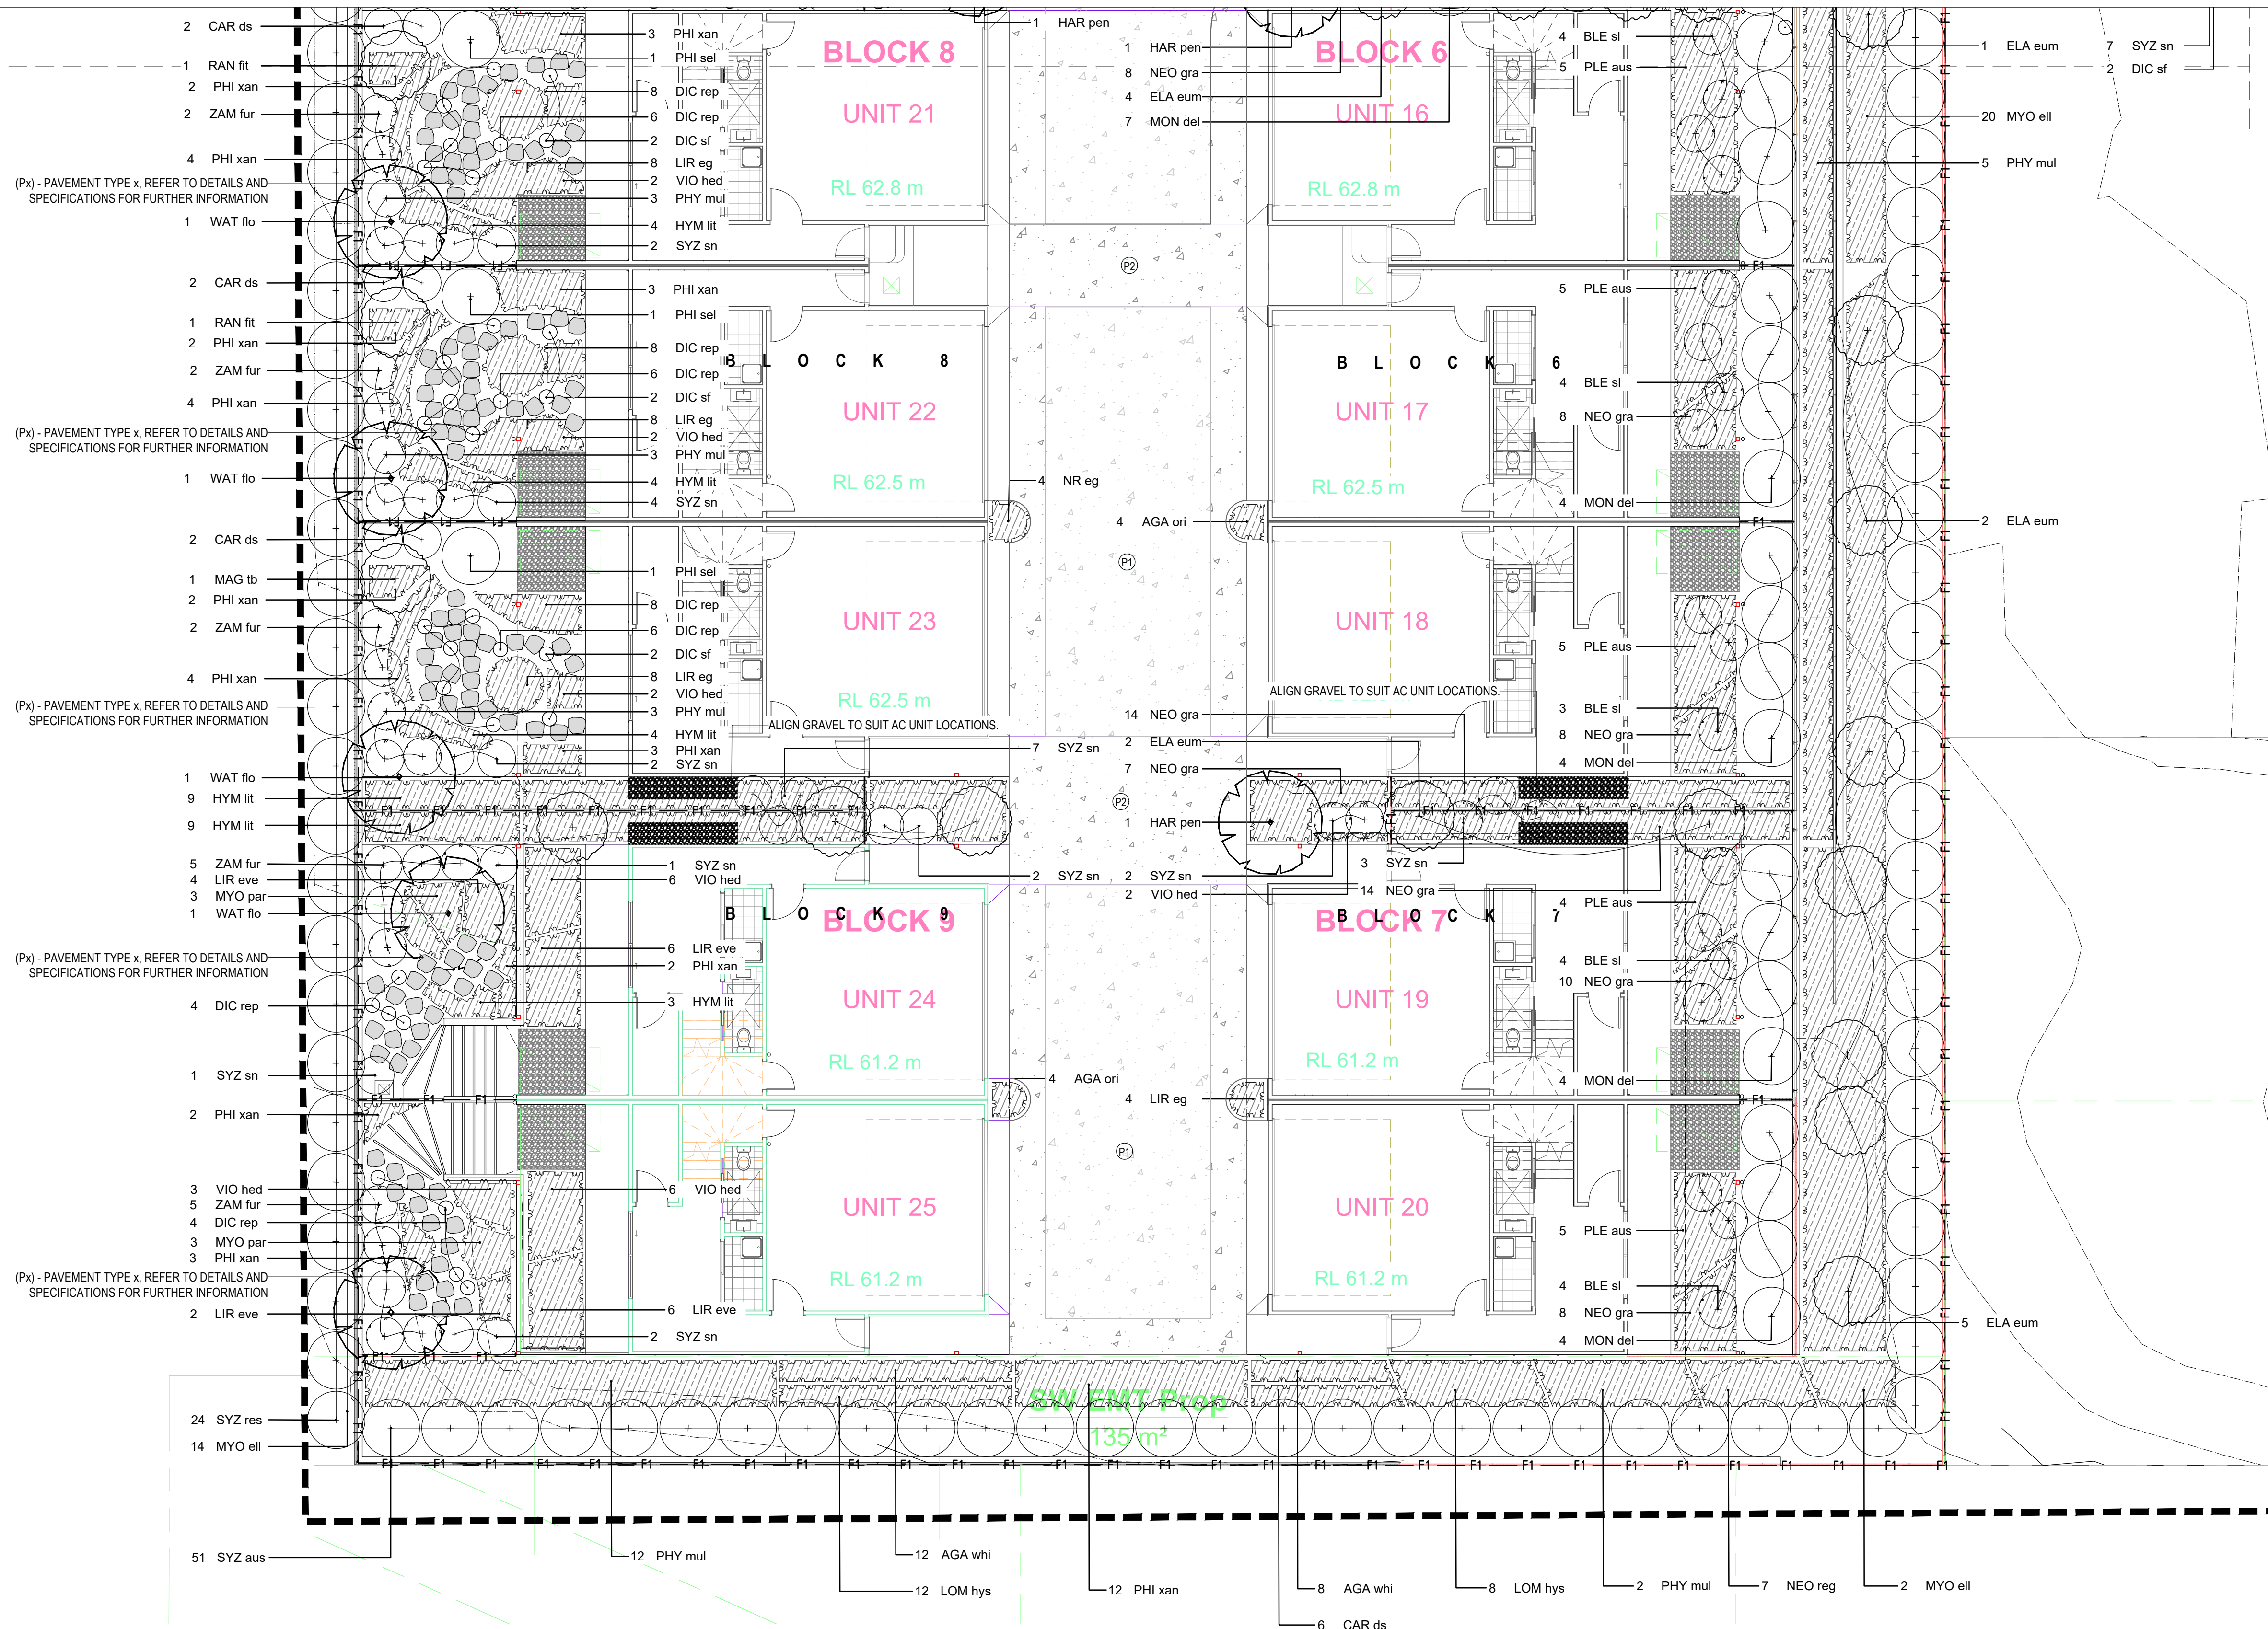

IMPORTANT NOTES:
This plan was prepared for GROOVE PROPERTIES PTY LTD
and should not be used for any other purpose.

The dimensions, areas and total number of lots shown hereon are subject to final field survey and also to the requirements of Council and any other authority which may have requirements under any relevant legislation.


The Contours, boundaries, creek line, flood lines, building locations have all been scaled and should not have any reliance based on them as they are only intended as a general guide. The configuration of allotments shown on this plan is subject to Local Authority (and relevant State Government Authority) approvals, detailed design, final survey, and registration of survey plans.

Any comments contained on this plan should be confirmed by the relevant authorities.
In particular, no relevance should be placed on the information on this plan for any financial dealings involving the land.

(C) COPYRIGHT THE LANDSCAPE GROUP: 2024

**THESE DESIGNS AND DRAWINGS ARE COPYRIGHT
AND ARE NOT TO BE USED OR REPRODUCED
WITHOUT THE WRITTEN PERMISSION OF THE
LANDSCAPE GROUP**

**REFER TO ARCHITECTURAL & ENGINEERING
DRAWINGS FOR LOCATIONS OF SERVICES**

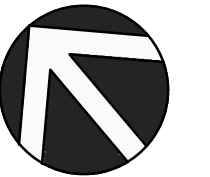

A	Design Issue	XX.12.2024	D5
No	Revisions	Date	Chkd

Locality: EVERTON HILLS
Local Authority: M.B.R.C
Scale: 1:100 @ A1
1:200 @ A3

Drawn: KD
Checked: DS
Plot Date: XX DEC, 2024
Computer File Ref: D23021-LP-A.dwg


DETAILED LANDSCAPE WORKS

**LANDSCAPE PLAN
SHEET 01 OF 02**




David Scassola AILA
REGISTERED LANDSCAPE ARCHITECT
Membership #: 001846
PH: 0407 589 785
EMAIL: david@thelandscapegroup.com.au
ABN: 83166834224


Drawing No	Issue
D24066-LP-04	A

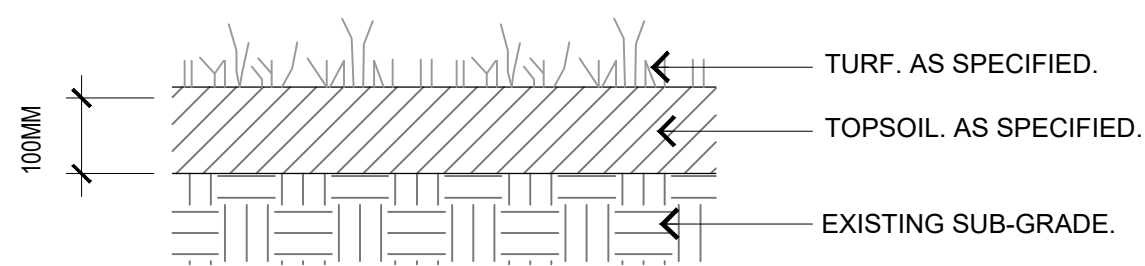


LD01 TYPICAL TURF DETAIL
1:10@A1

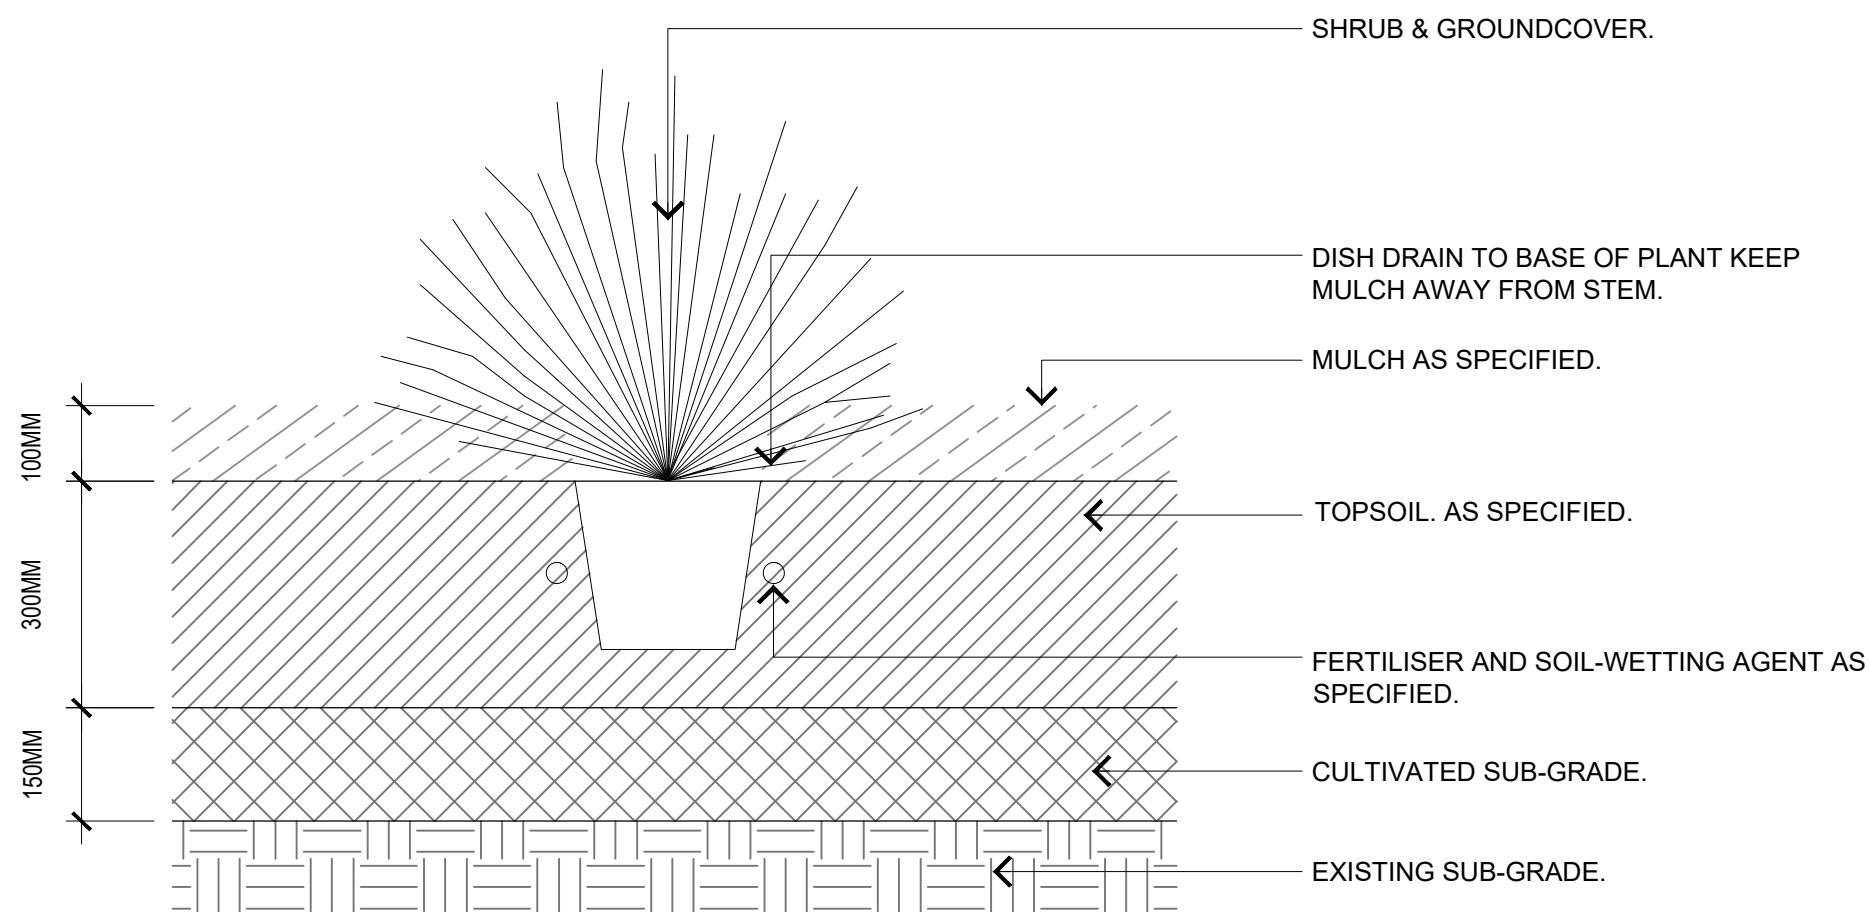


LD02 TYPICAL PLANTING DETAIL
1:10@A1

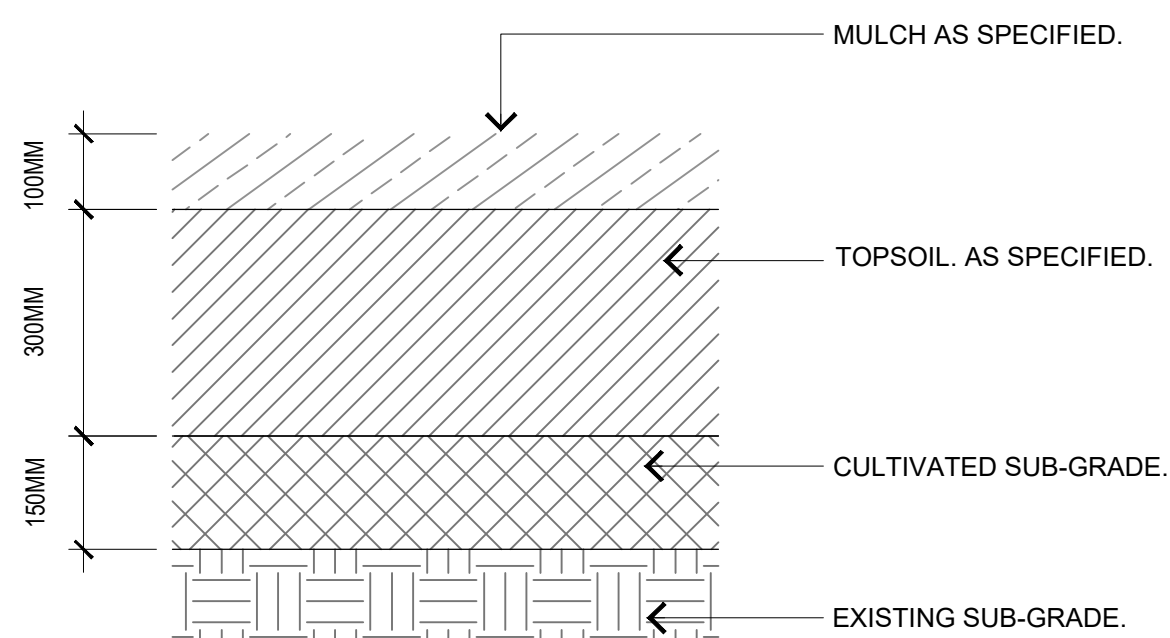

LD03 TYPICAL MULCH DETAIL
1:10@A1

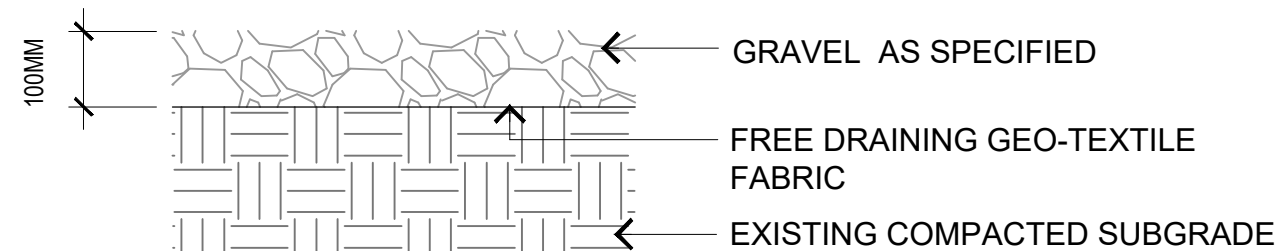


LD04 TYPICAL GRAVEL MULCH DETAIL
1:10@A1

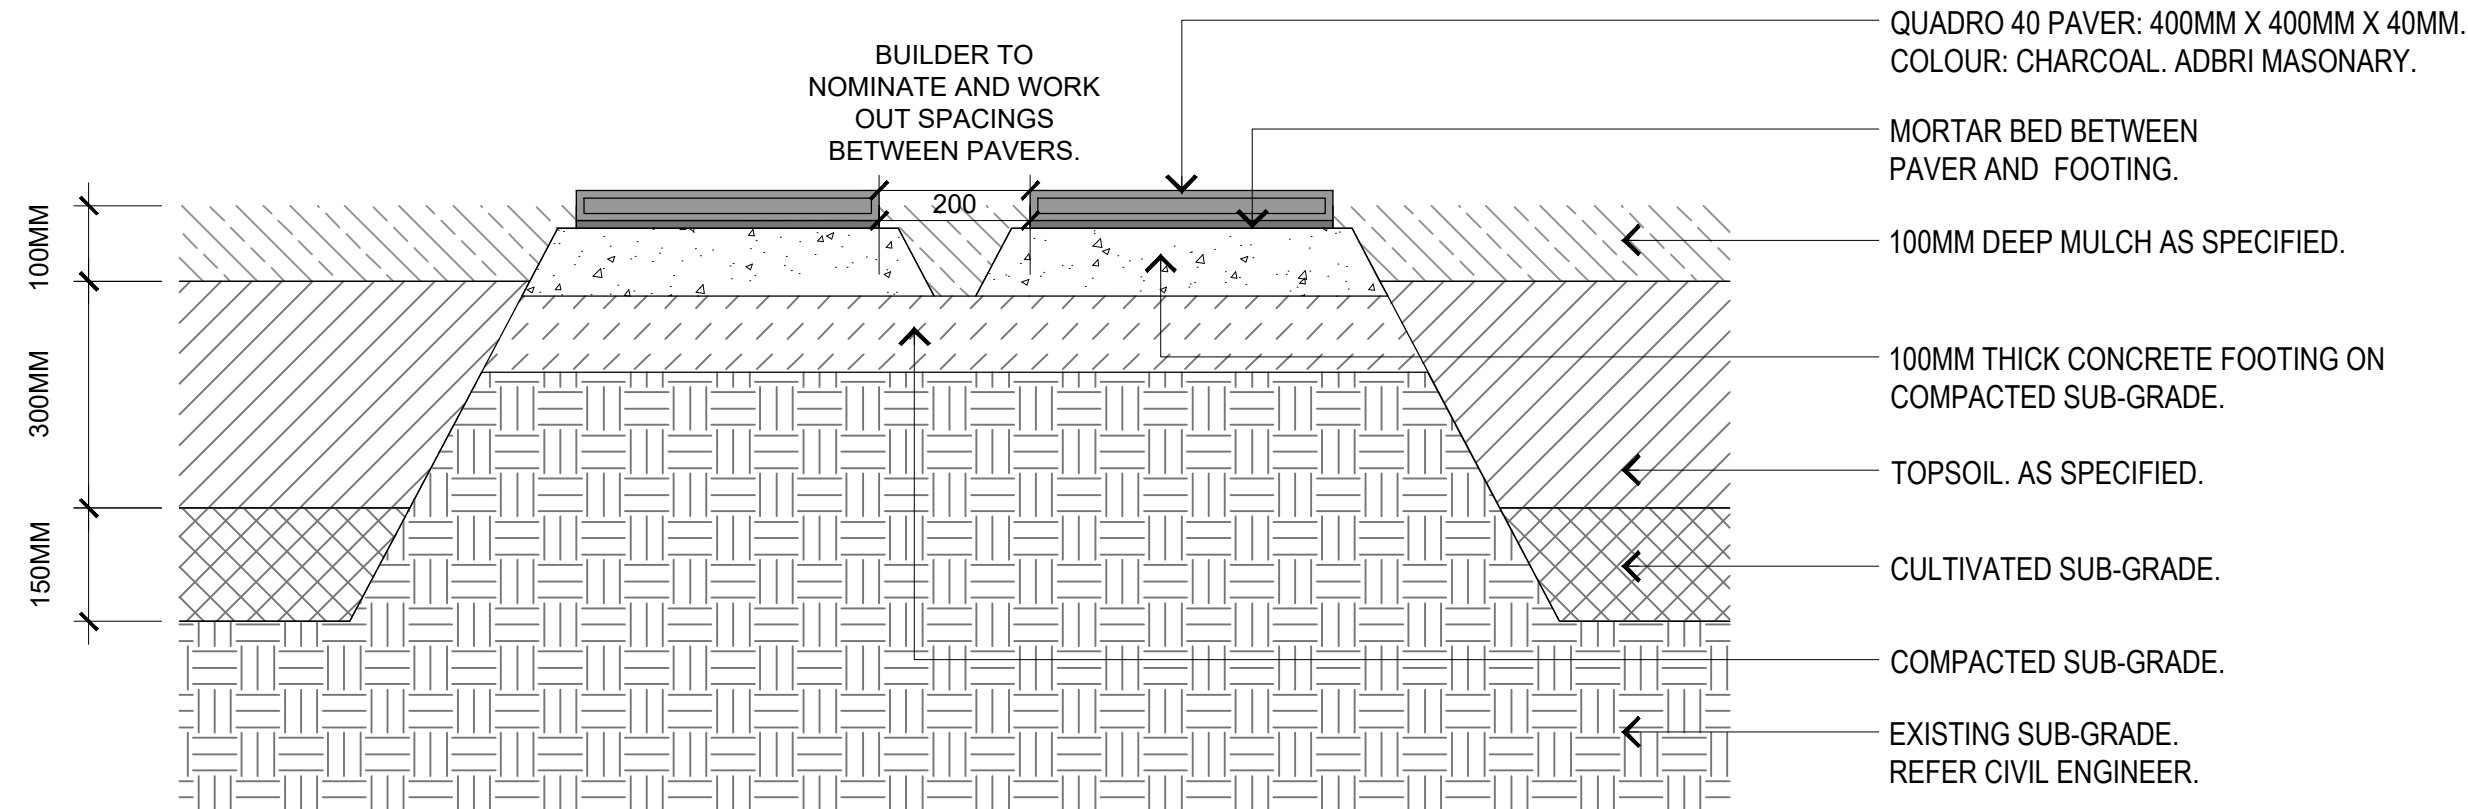

SPECIFICATION NOTES

- 1. Compacted Sub-grade:**
Compact the existing sub-grade material to 95% AASHO modified. Where the existing sub-grade is not suitable for compaction, excavate and replace with suitable fill material, which will achieve the specified rate of compaction.
- 2. Cultivated Sub-grade:**
Cultivate existing sub-grade to a depth of 200mm minimum.
- 3. Topsoil:**
Supply and install 300mm minimum depth Imported Garden Blend/Topsoil to AS 4419.
- 4. Mulch:**
Supply and install 75mm minimum depth Imported Organic Mulch (Note: HWD Chip not acceptable).

LD01 CONCRETE PAVERS IN GRAVEL / GARDEN
1:10@A1

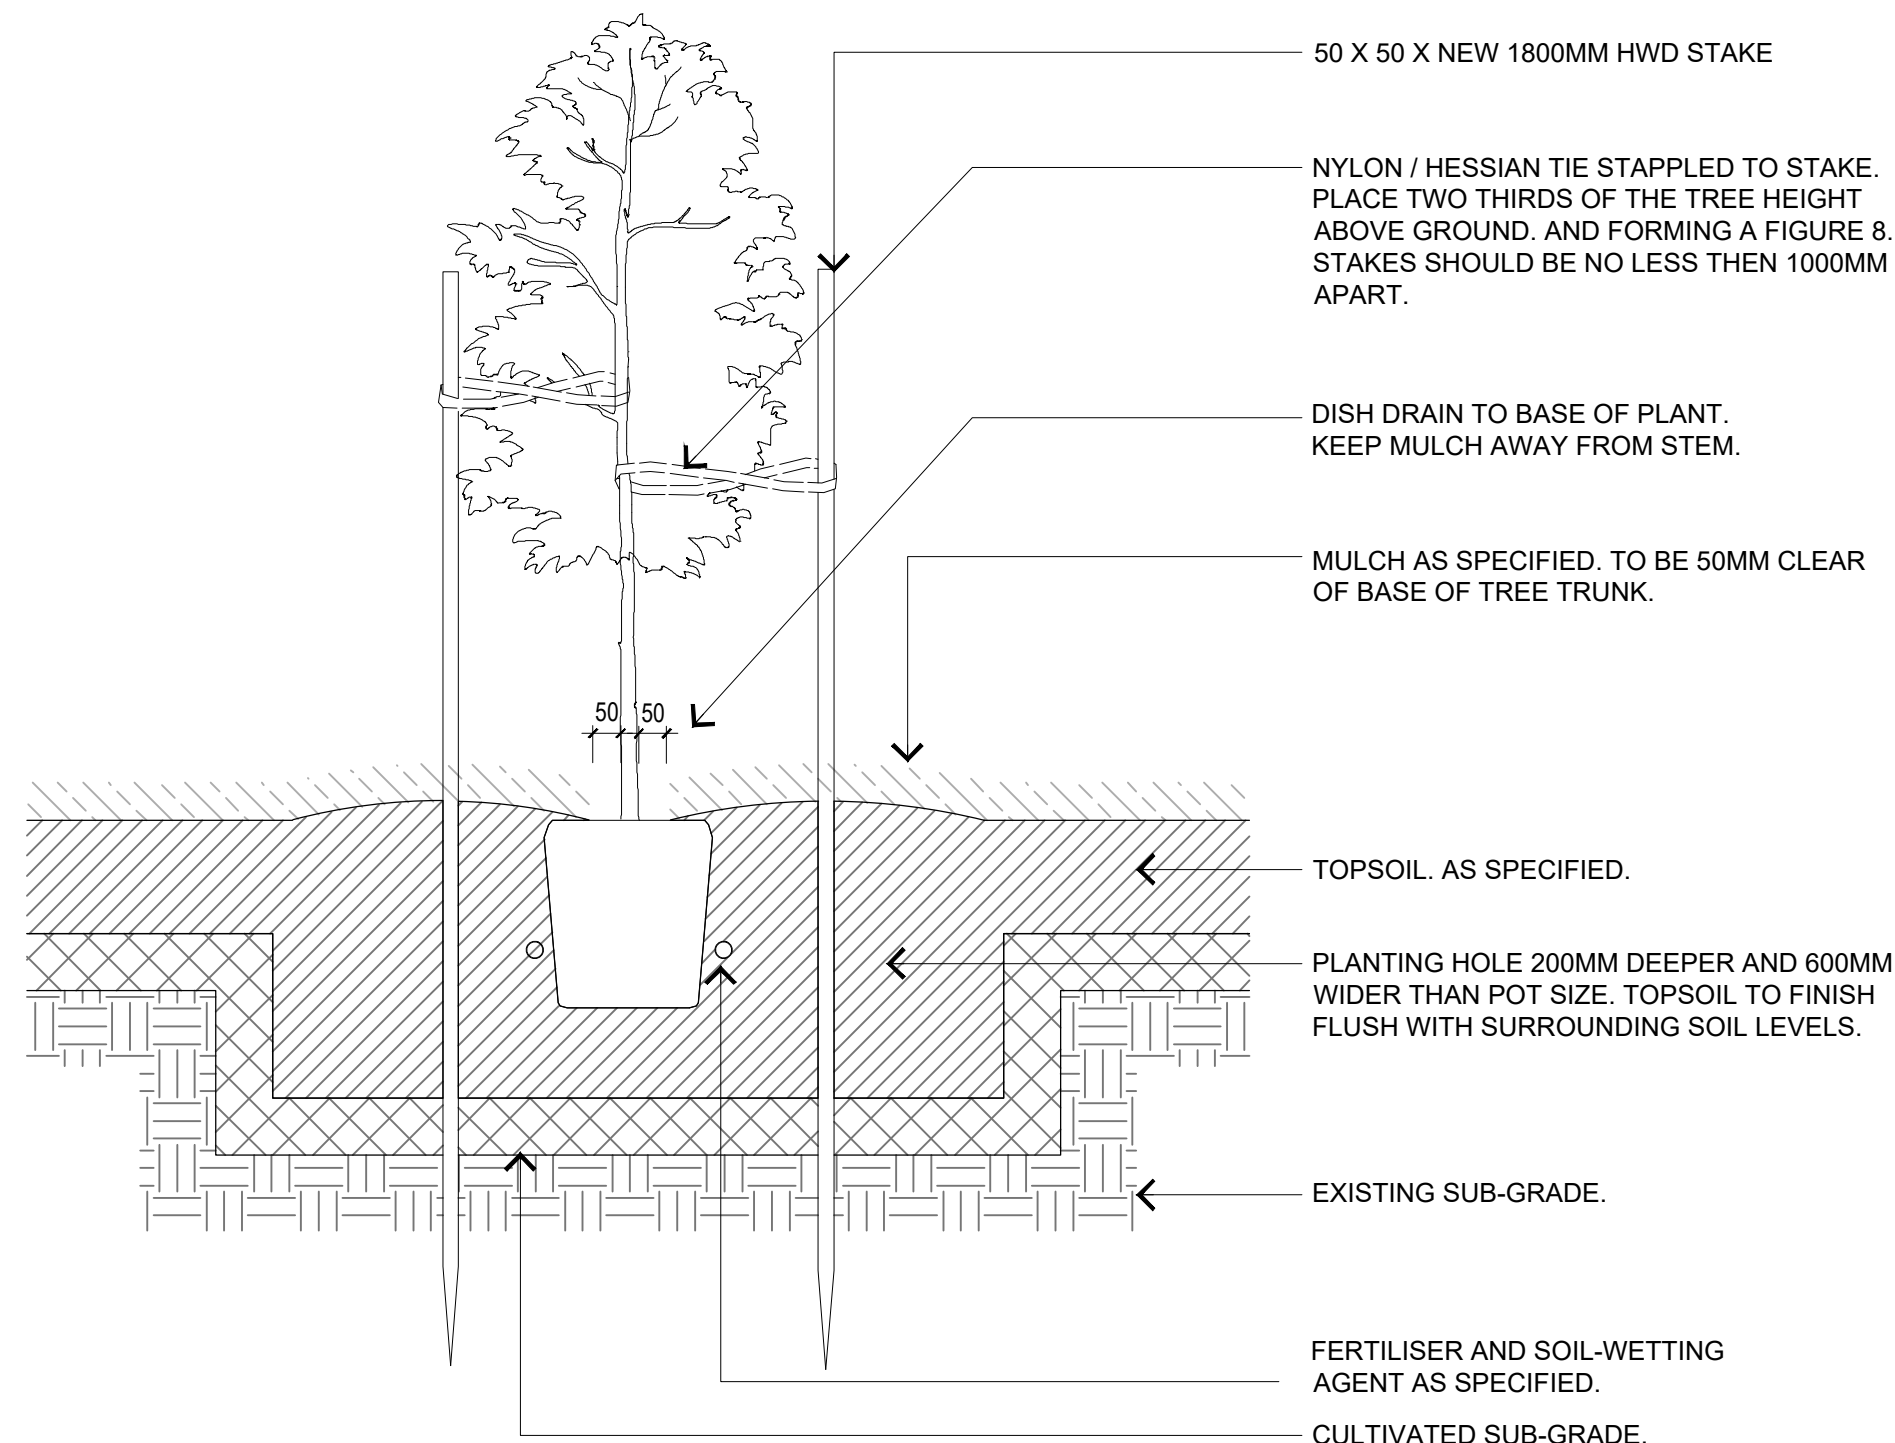

LD04 TYPICAL DETAIL: TREE PLANTING IN MULCH
1:20 @ A1

67-73 QUEENS RD
EVERTON HILLS

For
GROOVE PROPERTIES
PTY LTD

IMPORTANT NOTES:
This plan was prepared for GROOVE PROPERTIES PTY LTD and should not be used for any other purpose.

The dimensions, areas and total number of lots shown hereon are subject to final field survey and also to the requirements of Council and any other authority which may have requirements under any relevant legislation.

The Contours, boundaries, creek line, flood lines, building locations have all been scaled and should not have any reliance based on them as they are only intended as a general guide. The configuration of allotments shown on this plan is subject to Local Authority (and relevant State Government Authority) approvals, detailed design, final survey, and registration of survey plans.

Any comments contained on this plan should be confirmed by the relevant authorities. In particular, no relevance should be placed on the information on this plan for any financial dealings involving the land.

(C) COPYRIGHT THE LANDSCAPE GROUP: 2024

THESE DESIGNS AND DRAWINGS ARE COPYRIGHT AND ARE NOT TO BE USED OR REPRODUCED WITHOUT THE WRITTEN PERMISSION OF THE LANDSCAPE GROUP

REFER TO ARCHITECTURAL & ENGINEERING DRAWINGS FOR LOCATIONS OF SERVICES

A	Design Issue	XX.12.2024	DS
No	Revisions	Date	Chkd

Locality: EVERTON HILLS
Local Authority: M.B.R.C
Scale:

Drawn: KD
Checked: DS
Plot Date: XX DEC, 2024
Computer File Ref: D23021-LP-A.dwg

LANDSCAPE DETAILS



David Scassola AILA
REGISTERED LANDSCAPE ARCHITECT
Membership #: 001846
PH: 0407 589 785
EMAIL: david@thelandscapegroup.com.au
ABN: 83166834224

Drawing No
D24066DT-901

Issue
A